



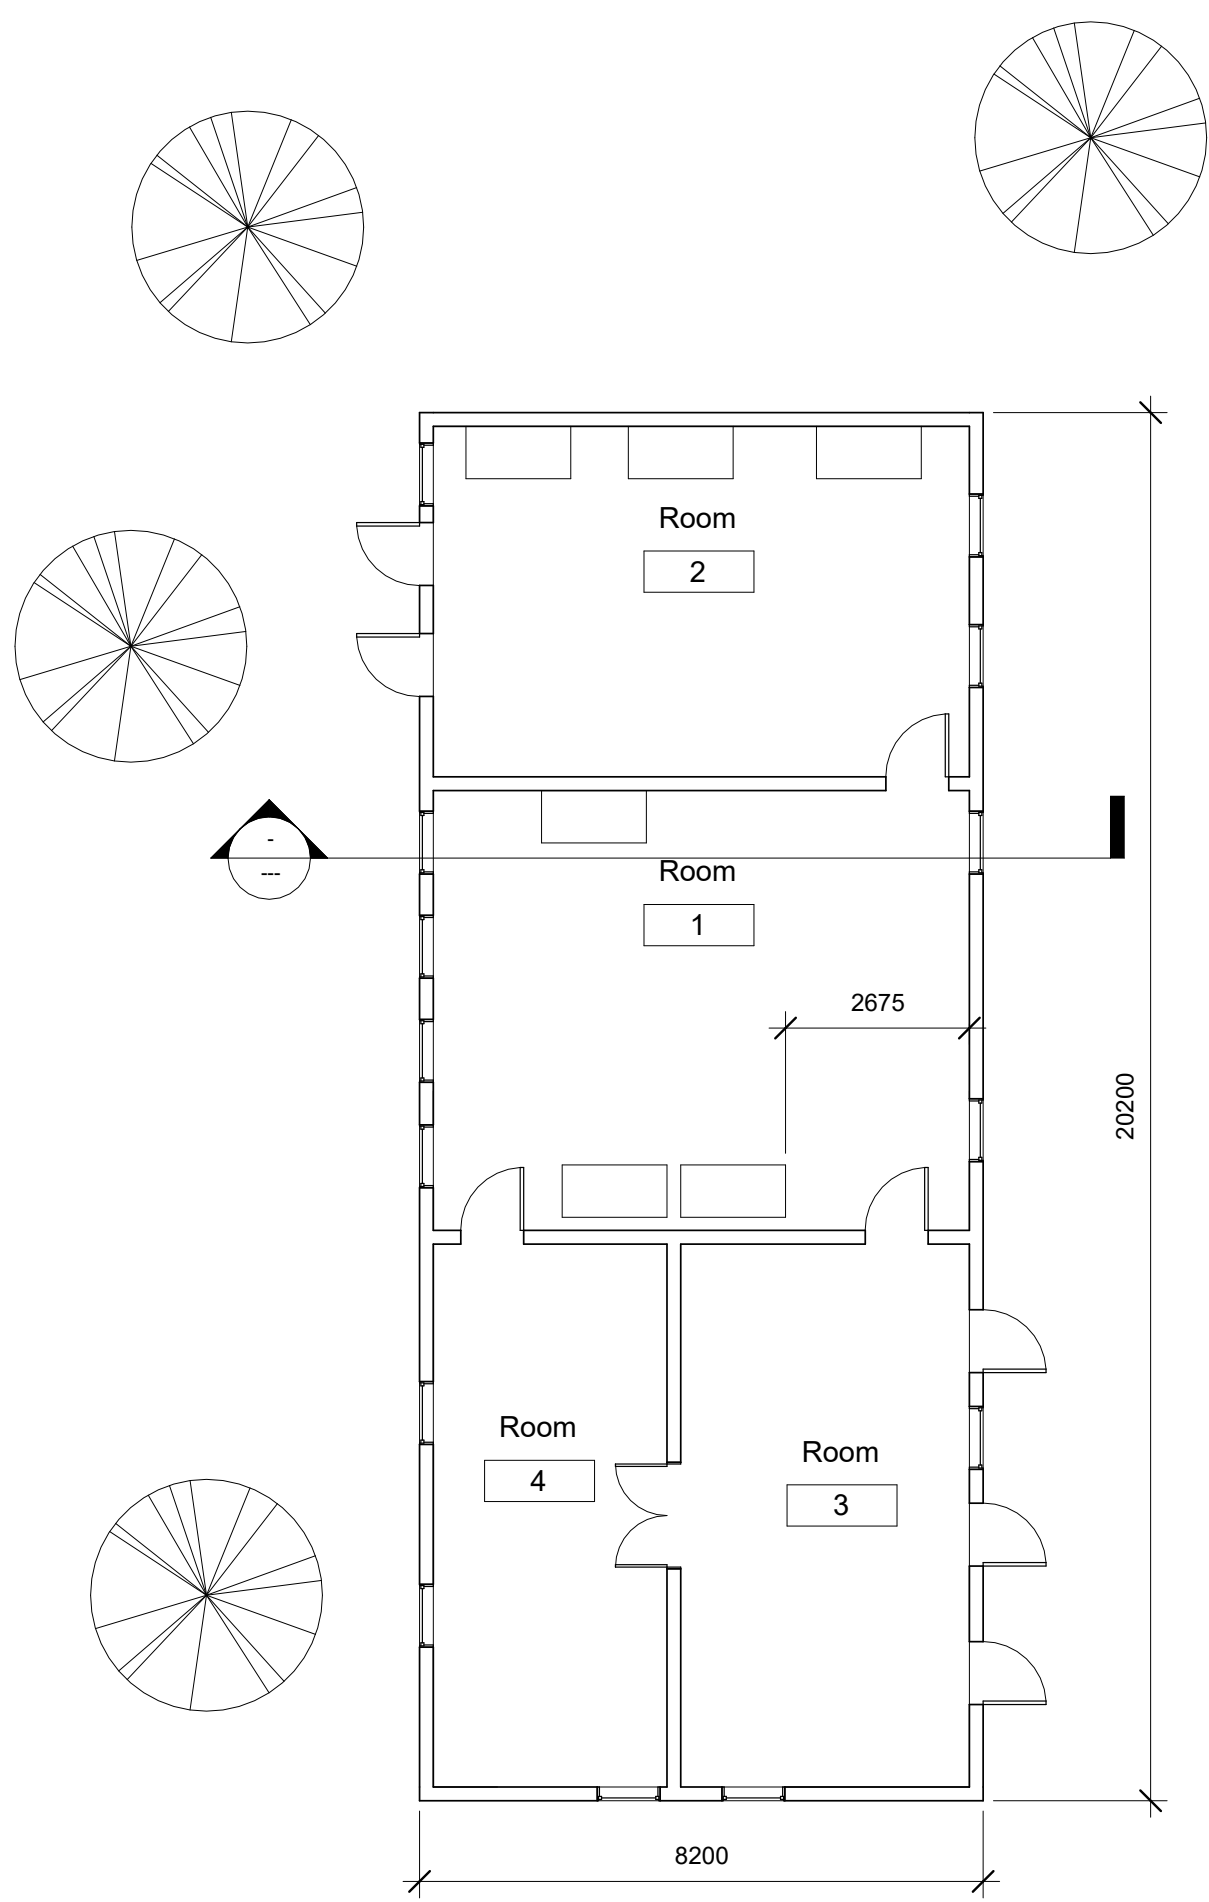

Large building A

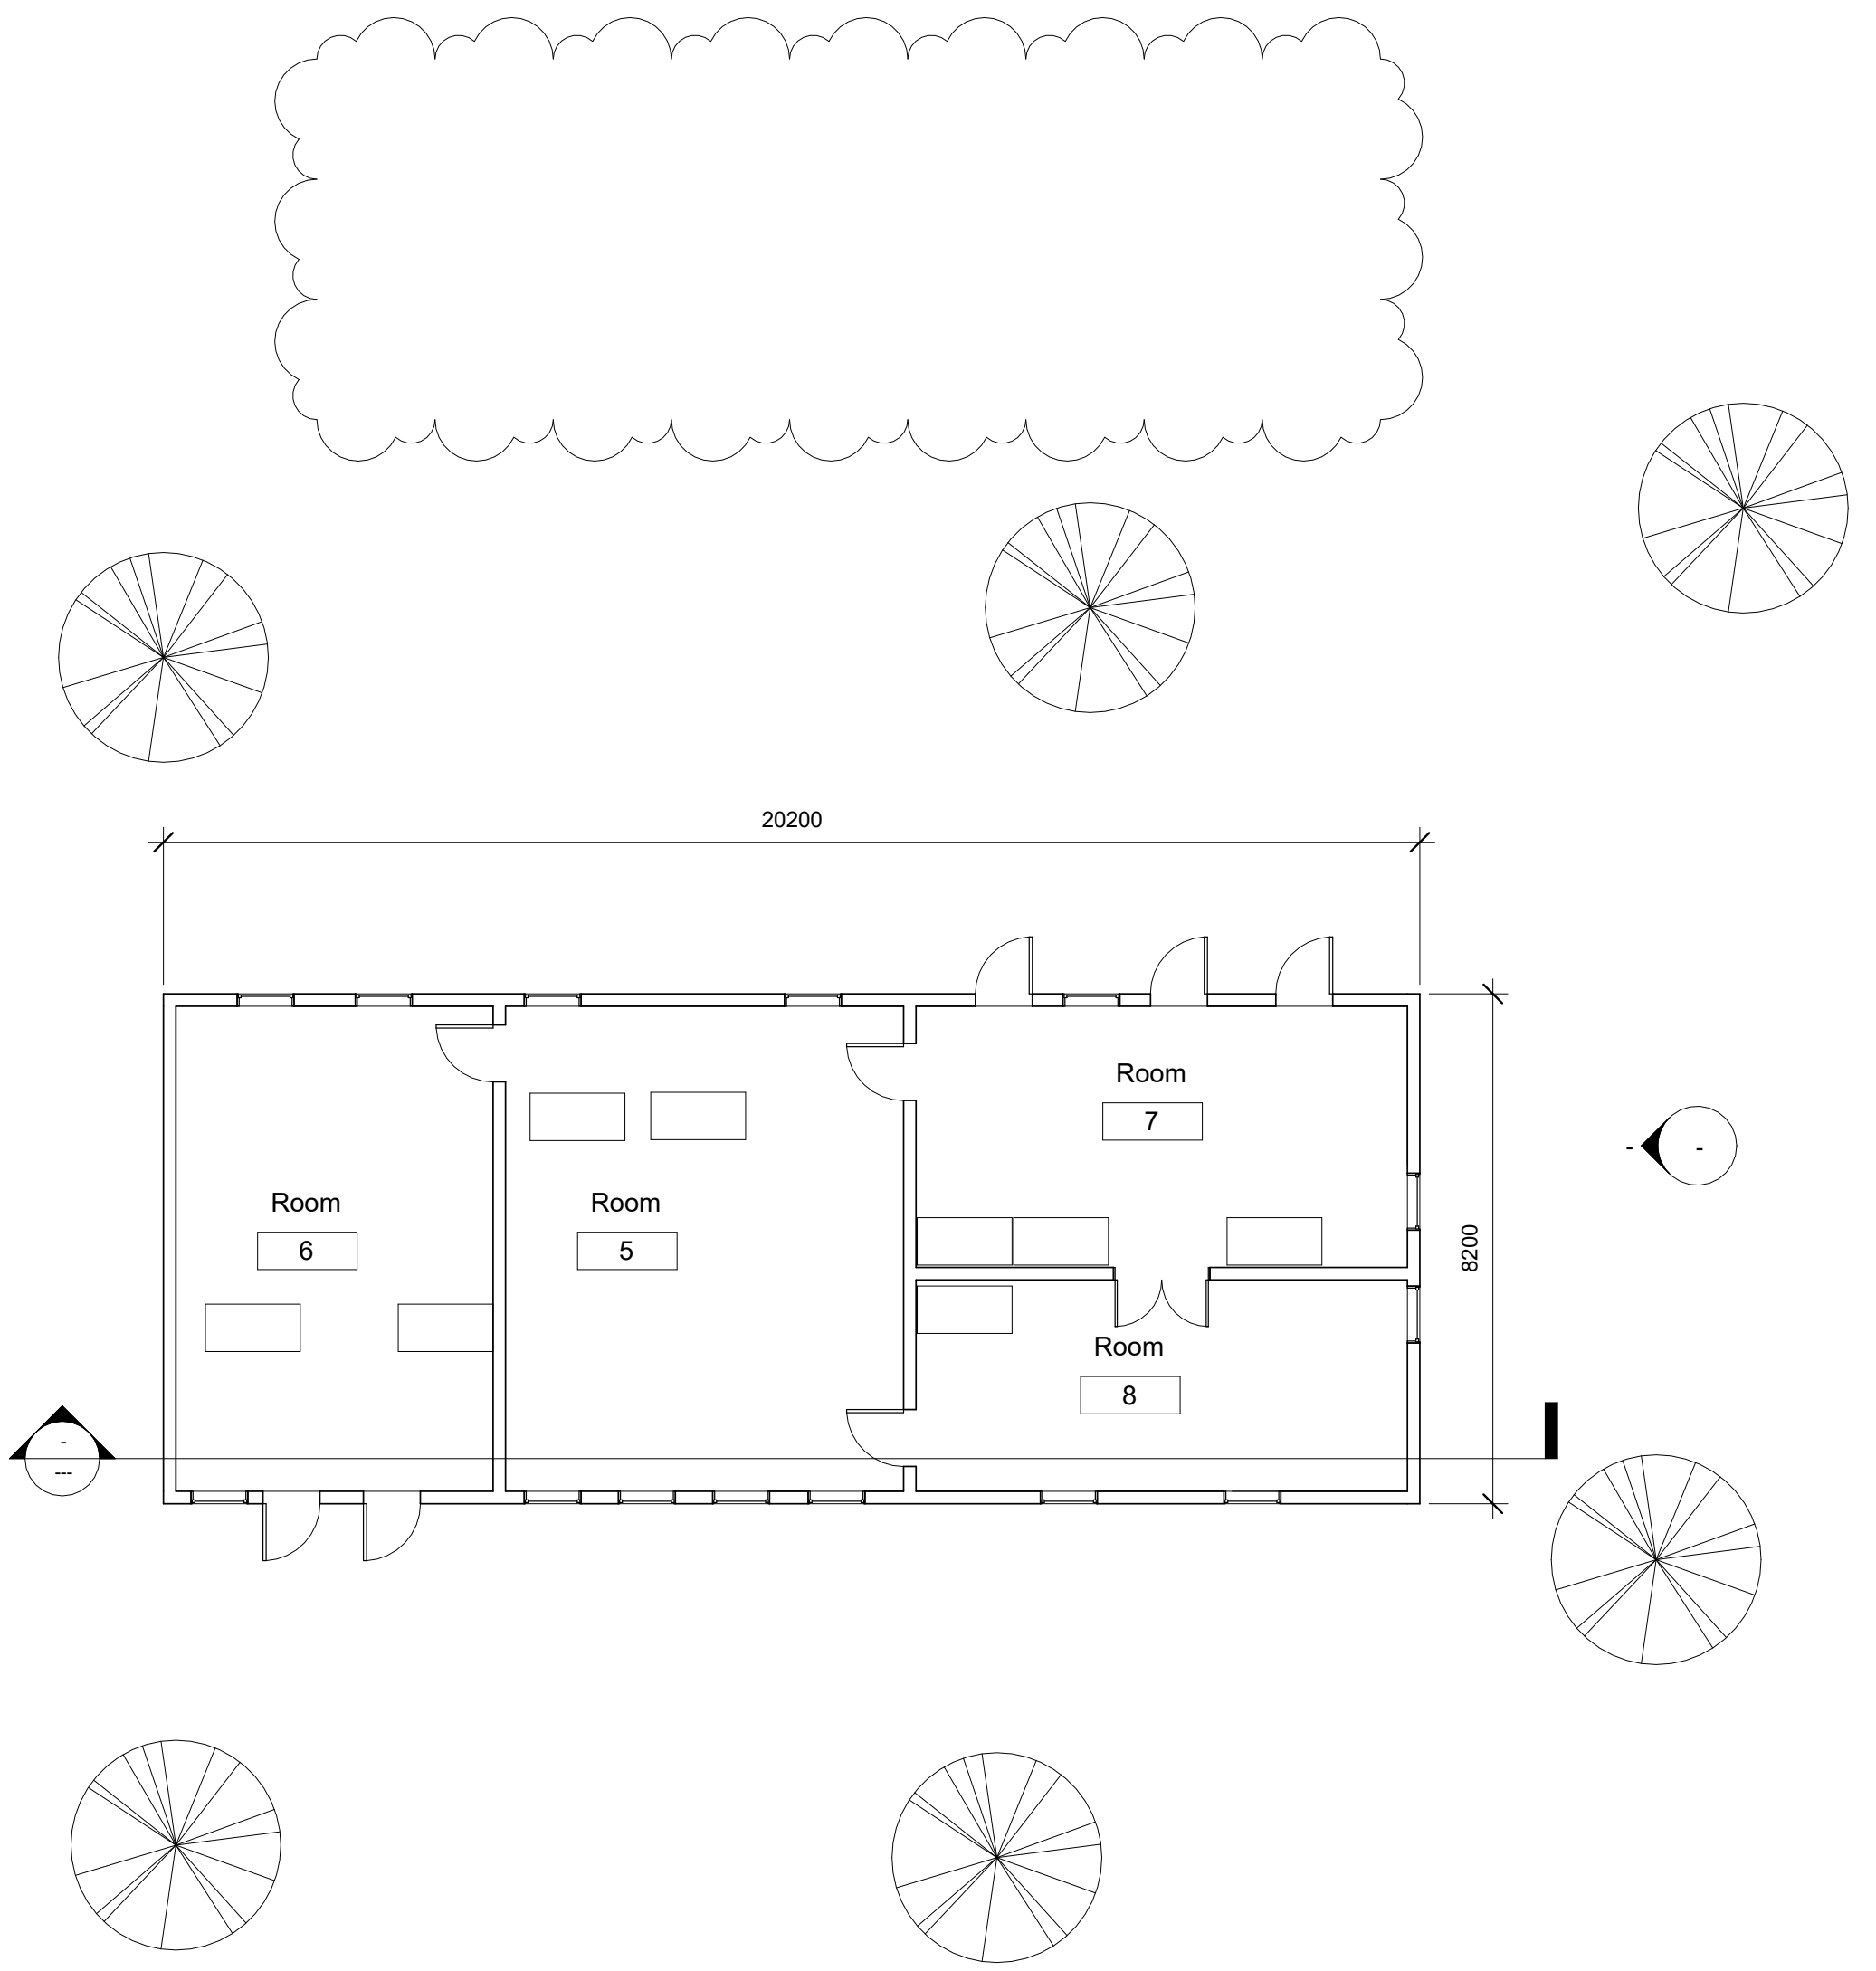

Large building B